



SAMPLE REPORT — reference design, not your parklet

CURBSIDE

Schematic parklet design for Vancouver streets

Sample parklet

Example street, Vancouver  
2026-10-03

Preliminary: not for construction

Checks: 19 pass, 0 fail,  
0 not confirmed

AI-assisted visualisation — indicative. Rendered with the author’s Replicate account for this sample; your own renders use the key you add in Connections.

ed visualisation – indicative

G-001 WHAT TO DO NEXT

[read this page and the cover](#)

Measure or confirm on site

Nothing: every value the checks read is measured or confirmed.

Failing checks

None.

A check passes only on measured or confirmed values; imported data gives a provisional result, estimates don't count.





## V-102 Sidewalk view

Camera: 49.5 mm lens, 20 deg to the deck axis - Nano Banana Pro (2K) - rendered 2026-09-25  
Rendered with the author's Replicate account for this sample; your own renders use the key you add in Connections.

AI-assisted visualisation — indicative

Sample - page 4/18



V-103 Corner view

Camera: 49.5 mm lens, 6 deg to the deck axis · Nano Banana Pro (2K) · rendered 2026-09-25  
Rendered with the author's Replicate account for this sample; your own renders use the key you add in Connections.



V-104 Aerial view

Camera: isometric, as the axonometric · Nano Banana Pro (2K) · rendered 2026-09-25  
Rendered with the author's Replicate account for this sample; your own renders use the key you add in Connections.

Curbside parklet drawing set

## Sample parklet

Example street, Vancouver

Lat 49.28270, lon -123.12070 - street bearing 0.0 deg - parklet on the east side

Checks: 19 pass, 0 fail, 0 not confirmed

**Preliminary: not for construction**



## Drawing list

| Sheet          | Title                                     | Scale |
|----------------|-------------------------------------------|-------|
| V-000          | Cover                                     | NTS   |
| G-001          | What to do next                           |       |
| V-101 to V-104 | Renders: Street, Sidewalk, Corner, Aerial | NTS   |
| A-000          | Title sheet                               | NTS   |
| A-101          | Site plan                                 | 1:250 |
| A-102          | Layout plan                               | 1:250 |
| A-103          | Deck plan                                 | 1:100 |
| A-201          | Street section                            | 1:100 |
| A-202          | Parklet section                           | 1:50  |
| S-001          | Furniture schedule                        |       |
| G-002          | Construction and budget                   |       |
| C-001          | Compliance                                |       |
| S-002          | Site survey                               |       |
| X-001          | Sources                                   |       |

## Revisions

| Rev | Date       | Description                                                                              |
|-----|------------|------------------------------------------------------------------------------------------|
| A   | 2026-10-03 | Preliminary issue for the Parklet Manual pre-application (generated by Curbside v0.17.2) |

### Legend
  
|                                                                                       |                                                 |
|---------------------------------------------------------------------------------------|-------------------------------------------------|
|    | Cut: deck, curb in section (0.70)               |
|    | Objects: deck edge, furniture (0.50)            |
|    | Edges: curbs, railing (0.35)                    |
|    | General (0.25)                                  |
|    | Context, dimensions (0.18)                      |
|    | Fine: hatching, grid (0.13)                     |
|    | Clearance zone (red: the check fails)           |
|    | Required distance, nothing measured: "req."     |
|    | Section line A-A, centre line                   |
|    | Match line, property line                       |
|    | Hidden, overhead, lane line                     |
|                                                                                       |                                                 |
|    | Fire hydrant                                    |
|    | Utility pole                                    |
|    | Signal controller box                           |
|    | Access chamber / manhole                        |
|    | Street tree canopy (genus tag)                  |
|                                                                                       |                                                 |
|    | Bus stop                                        |
|    | Grid line at a railing post                     |
|   | Level (datum: top of curb)                      |
|  | Key: its note in the sheet's notes              |
|  | Rule of a clearance zone                        |
|  | Clearance: measured · rule · check (red: fails) |
|                                                                                       |                                                 |
|  | Concrete                                        |
|  | Timber deck, along the boards                   |
|  | Planting                                        |
|  | Earth, subgrade                                 |
|  | Cut building                                    |
|  | Cut steel, thin material                        |
|  | Accessible route                                |

## Abbreviations

|           |                                                   |
|-----------|---------------------------------------------------|
| CO1 – C19 | Parklet Manual checks                             |
| CoV       | City of Vancouver (open data)                     |
| DBH       | diameter at breast height                         |
| EDM       | Engineering Design Manual                         |
| max / min | maximum / minimum                                 |
| NTS       | not to scale                                      |
| OSM       | OpenStreetMap                                     |
| typ.      | typical                                           |
| z         | distance along the street from the deck start (m) |

## Notes

- Dimensions in metres unless noted; drawings at the scale stated on a 17 x 11 in sheet.
- Generated from the design model; imported site data is indicative and must be verified on site.
- Sources, the renders' credits and the model's assumptions: sheet X-001.

A-000 Title sheet


Notes

- 1


Parklet, 19.80 m: layout A-102, deck A-103.
- 2

Section A-A: the street on A-201, the parklet on A-202.
- No street trees in this stretch.
- 3

Buildings from OpenStreetMap, cut at the sheet's extent (78.50 x 55.00 m); name and use where known.
- Site objects from City of Vancouver open data: indicative, confirm on site.

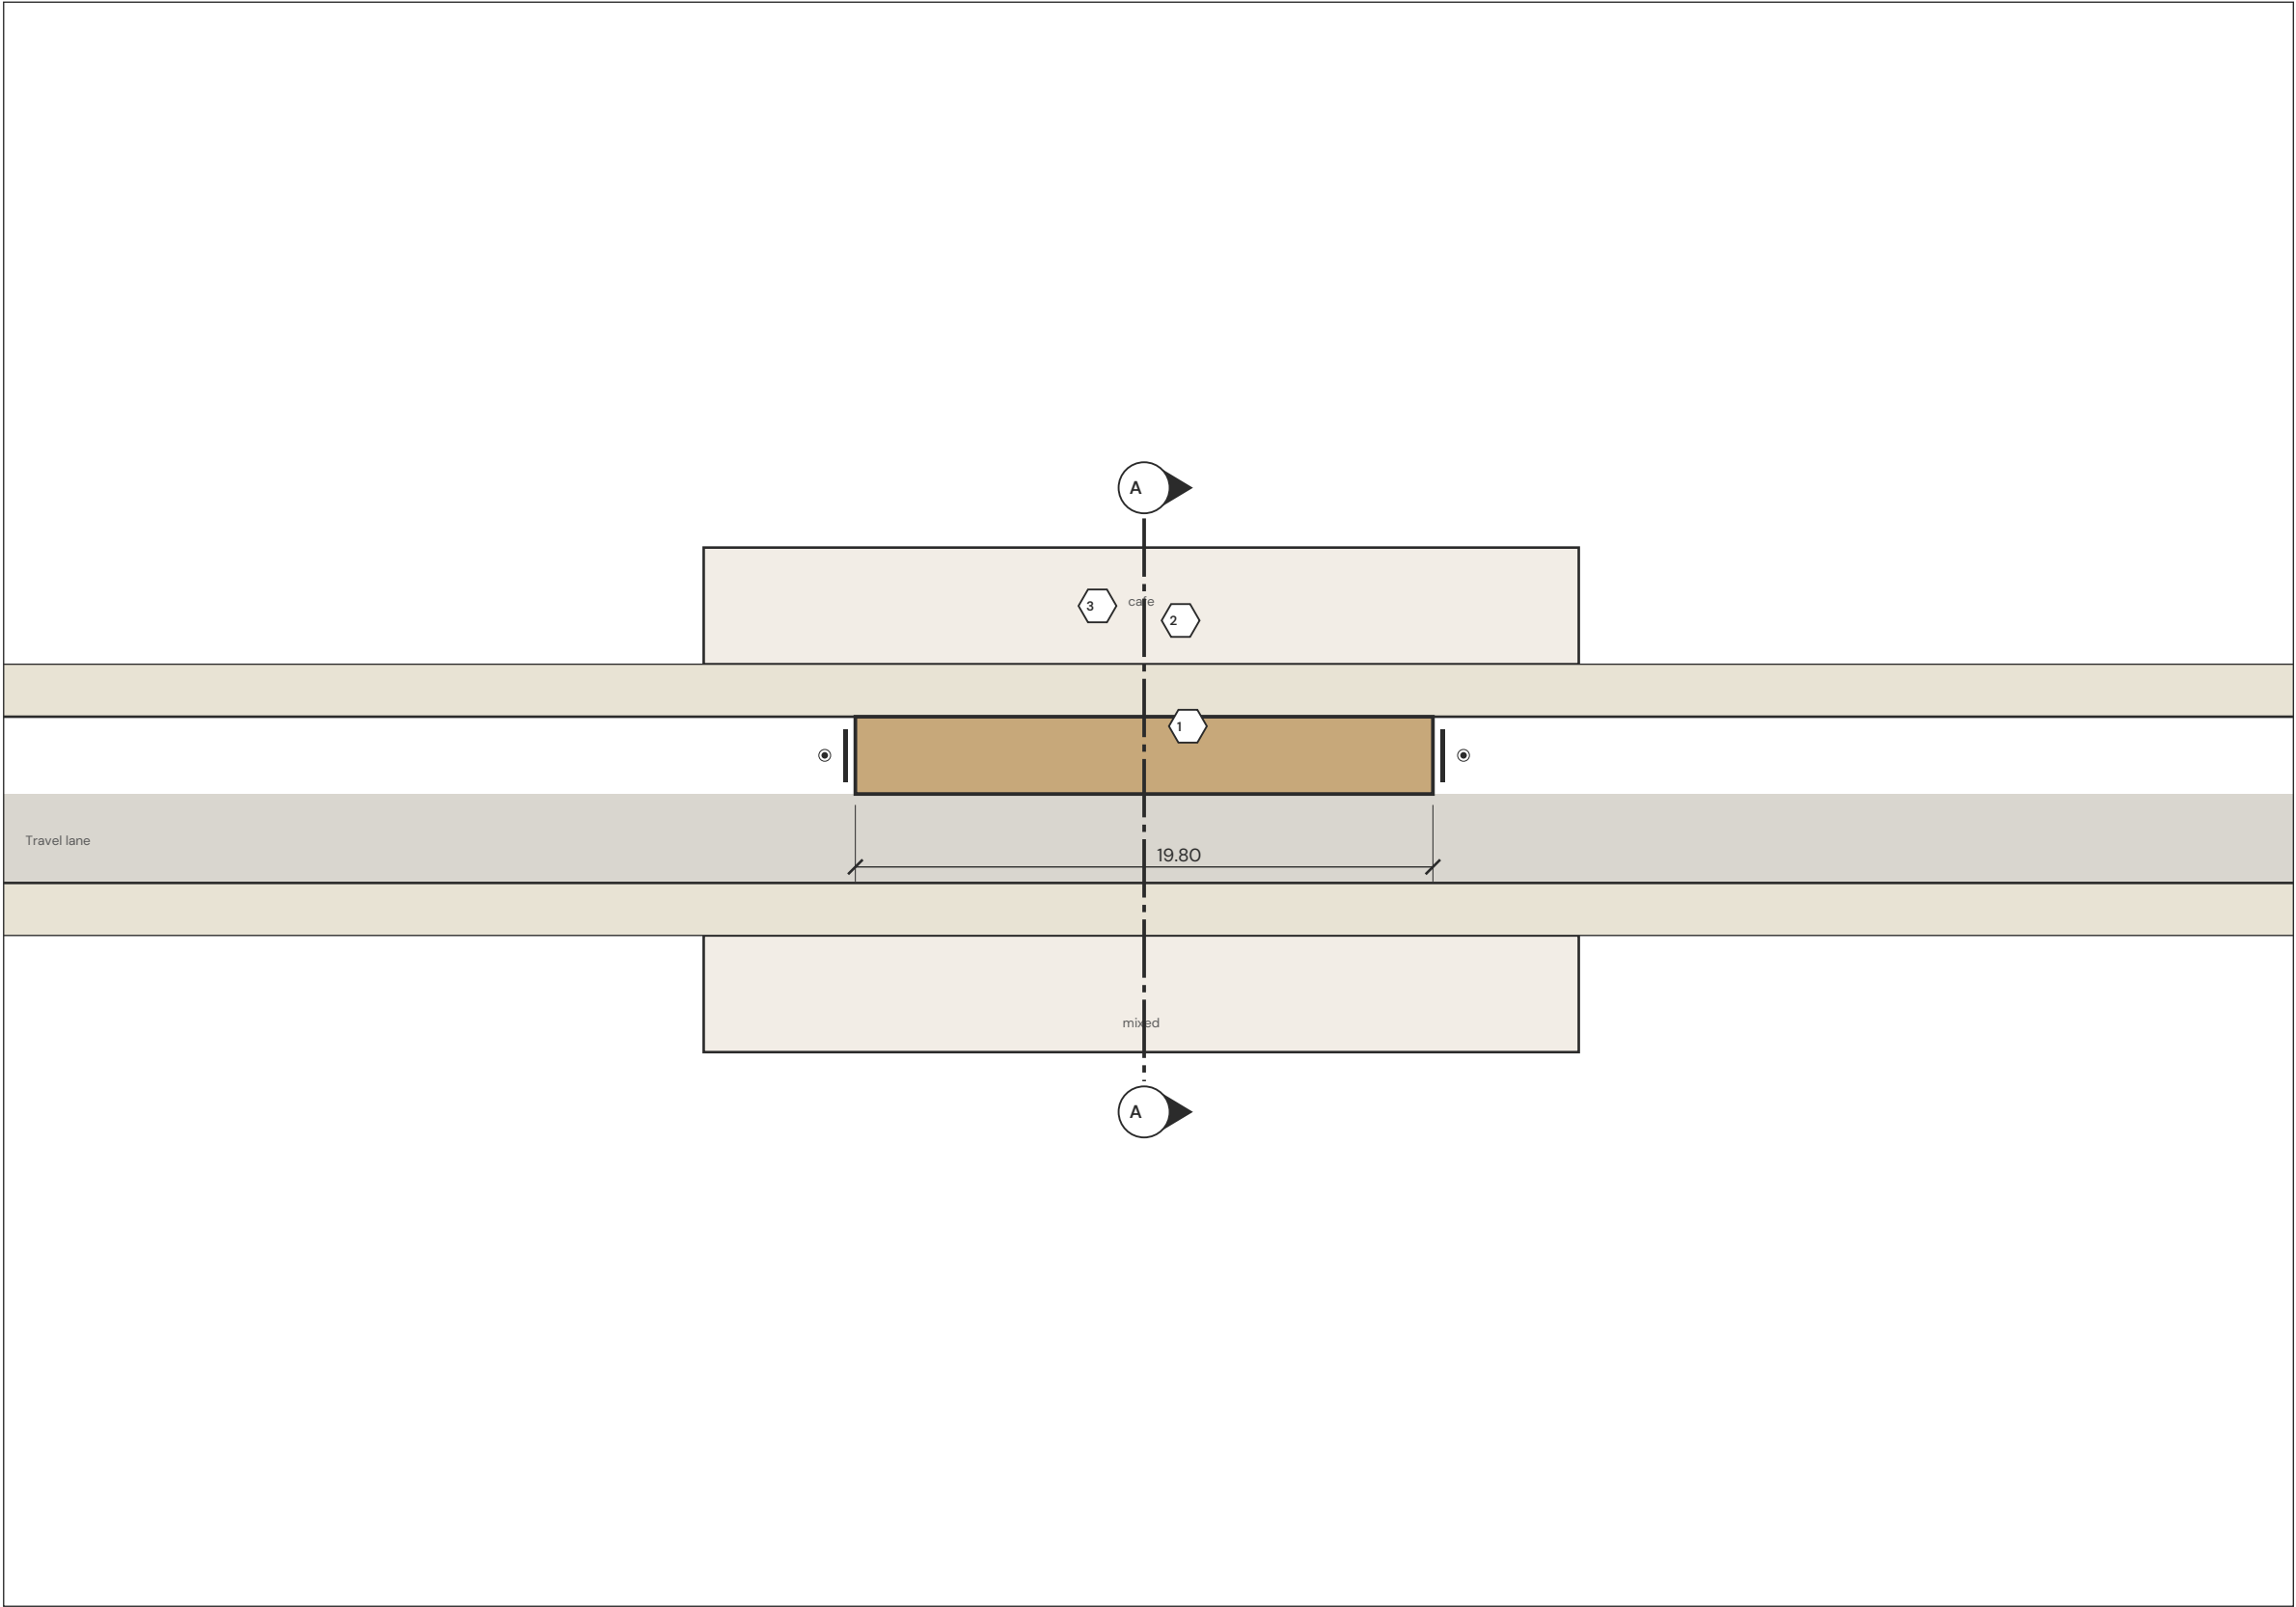

A-101 Site plan

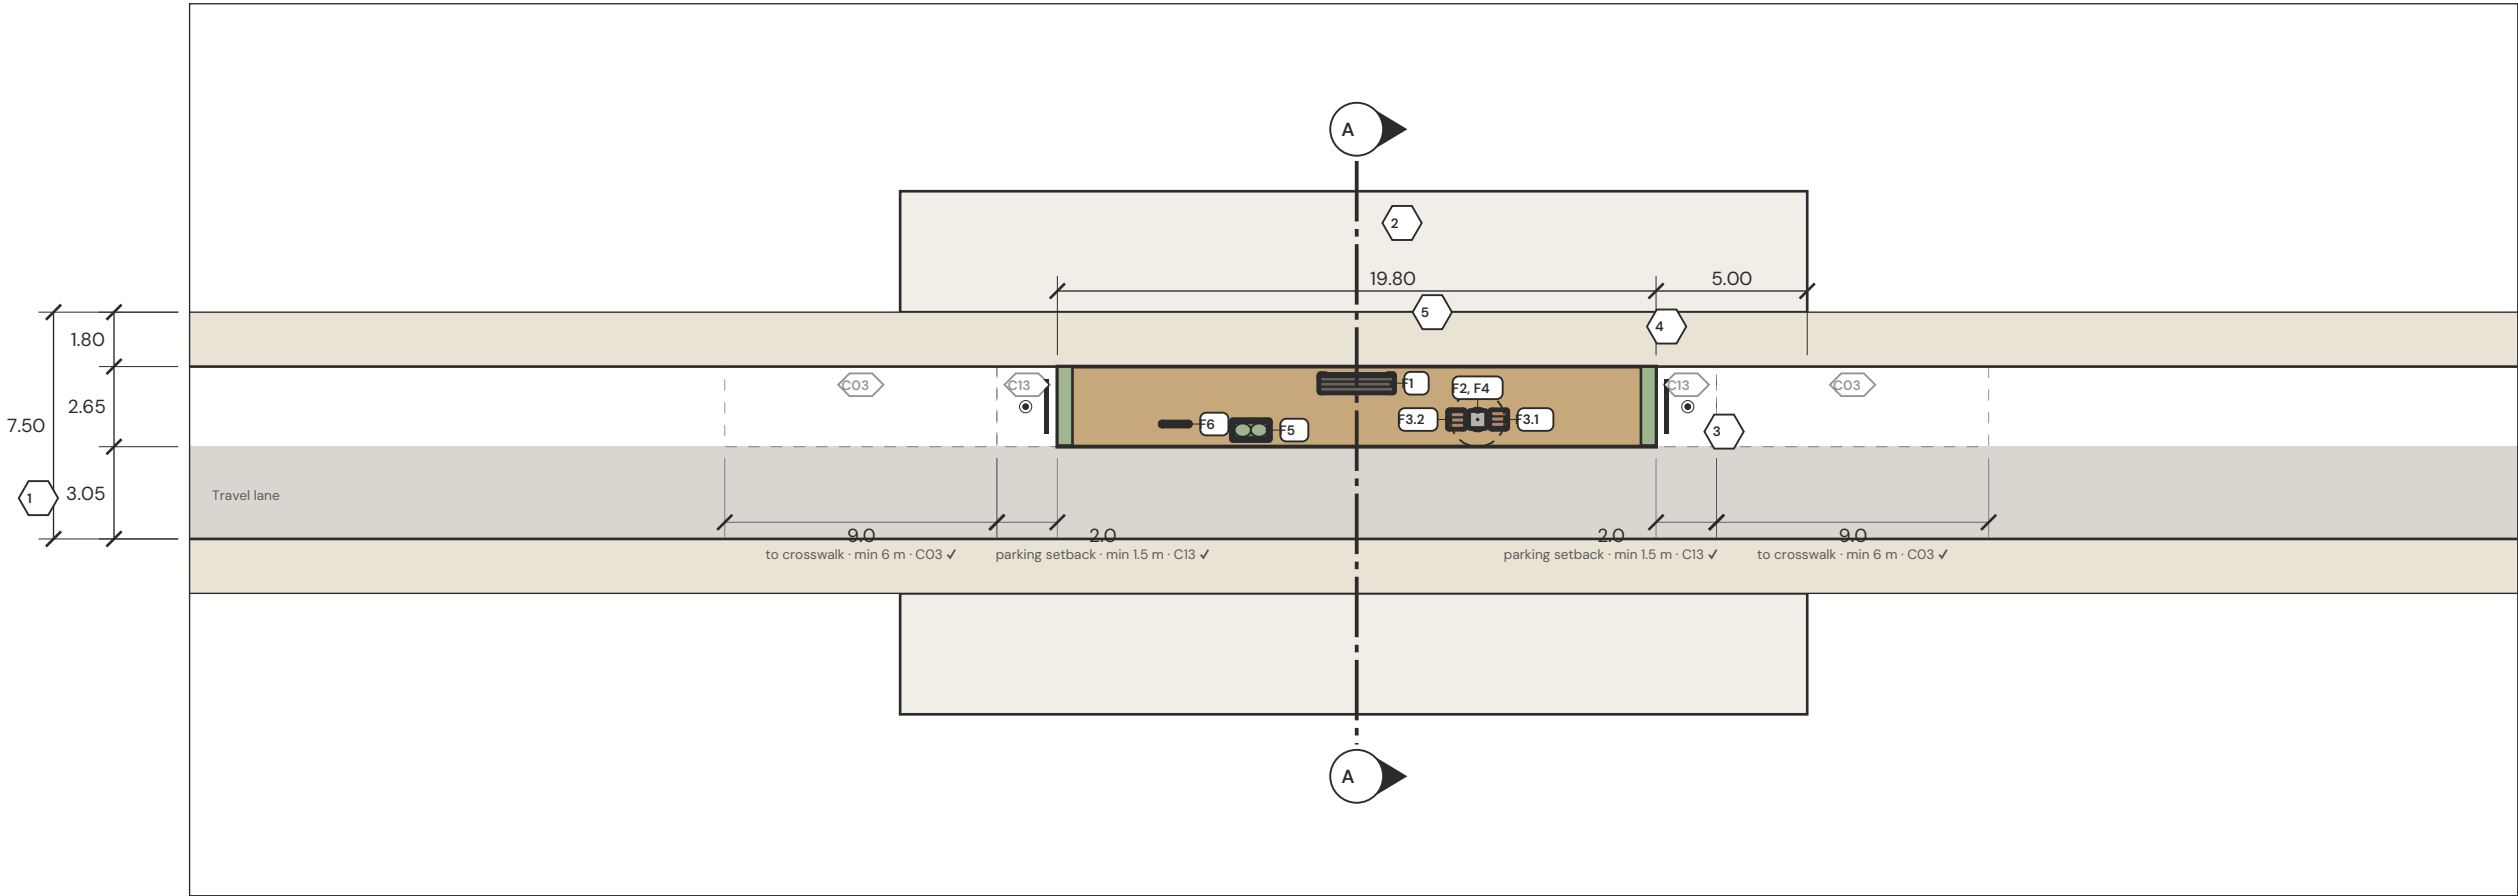


Notes

- 1 Segments from the Section editor, chained with the overall, frontage to far curb.
- 2 The deck located from the host frontage (cafe).
- 3 Clearance zones dashed, with their rule (C03 crosswalk, C05 hydrant, C07 pole, C08 signal, C09 chamber, C13 parking). Each clearance: measured, then rule and check beneath; red: the check fails.
  - Furniture tags: schedule S-001.
- 4 Wheel stop and flexible bollard at each end, supplied and installed by the City; location to City (Parklet Manual p. 48, 59).
- 5 Section A-A: the street on A-201, the parklet on A-202; deck plan A-103.



A-102 Layout plan

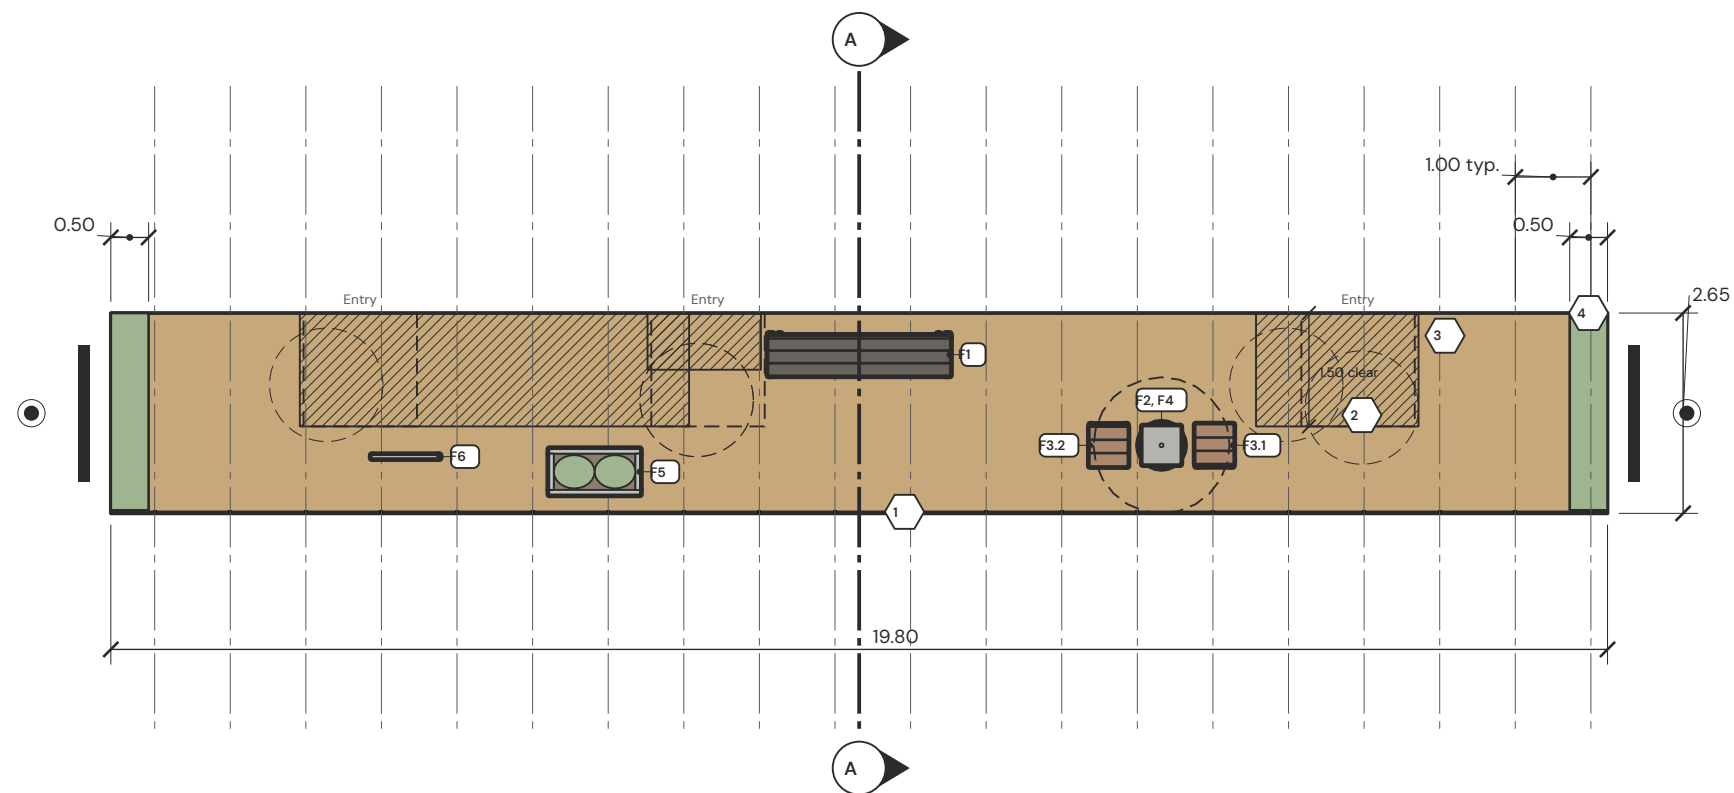


## Notes

- Grid lines 1, 2, 3 ... at the enclosure posts on the traffic side, 1.00 m apart, the first at 0.22 m.
- 1 Enclosure: steel picket in galvanized, 0.90 m high on the traffic side, at the deck edge; planter wall at both ends: in section on A-202.
- 2 Accessible route (C16), hatched: 1.50 m clear from each entry to an accessible seat; dashed circles: 1.50 m turning space where it turns and ends.
- 3 Entry: 1.50 m turning square at the sidewalk edge (C16).
- 4 End enclosure: planter wall, 0.50 m deep, 0.90 m high.
- Furniture tags: schedule S-001.



**A-103 Deck plan**

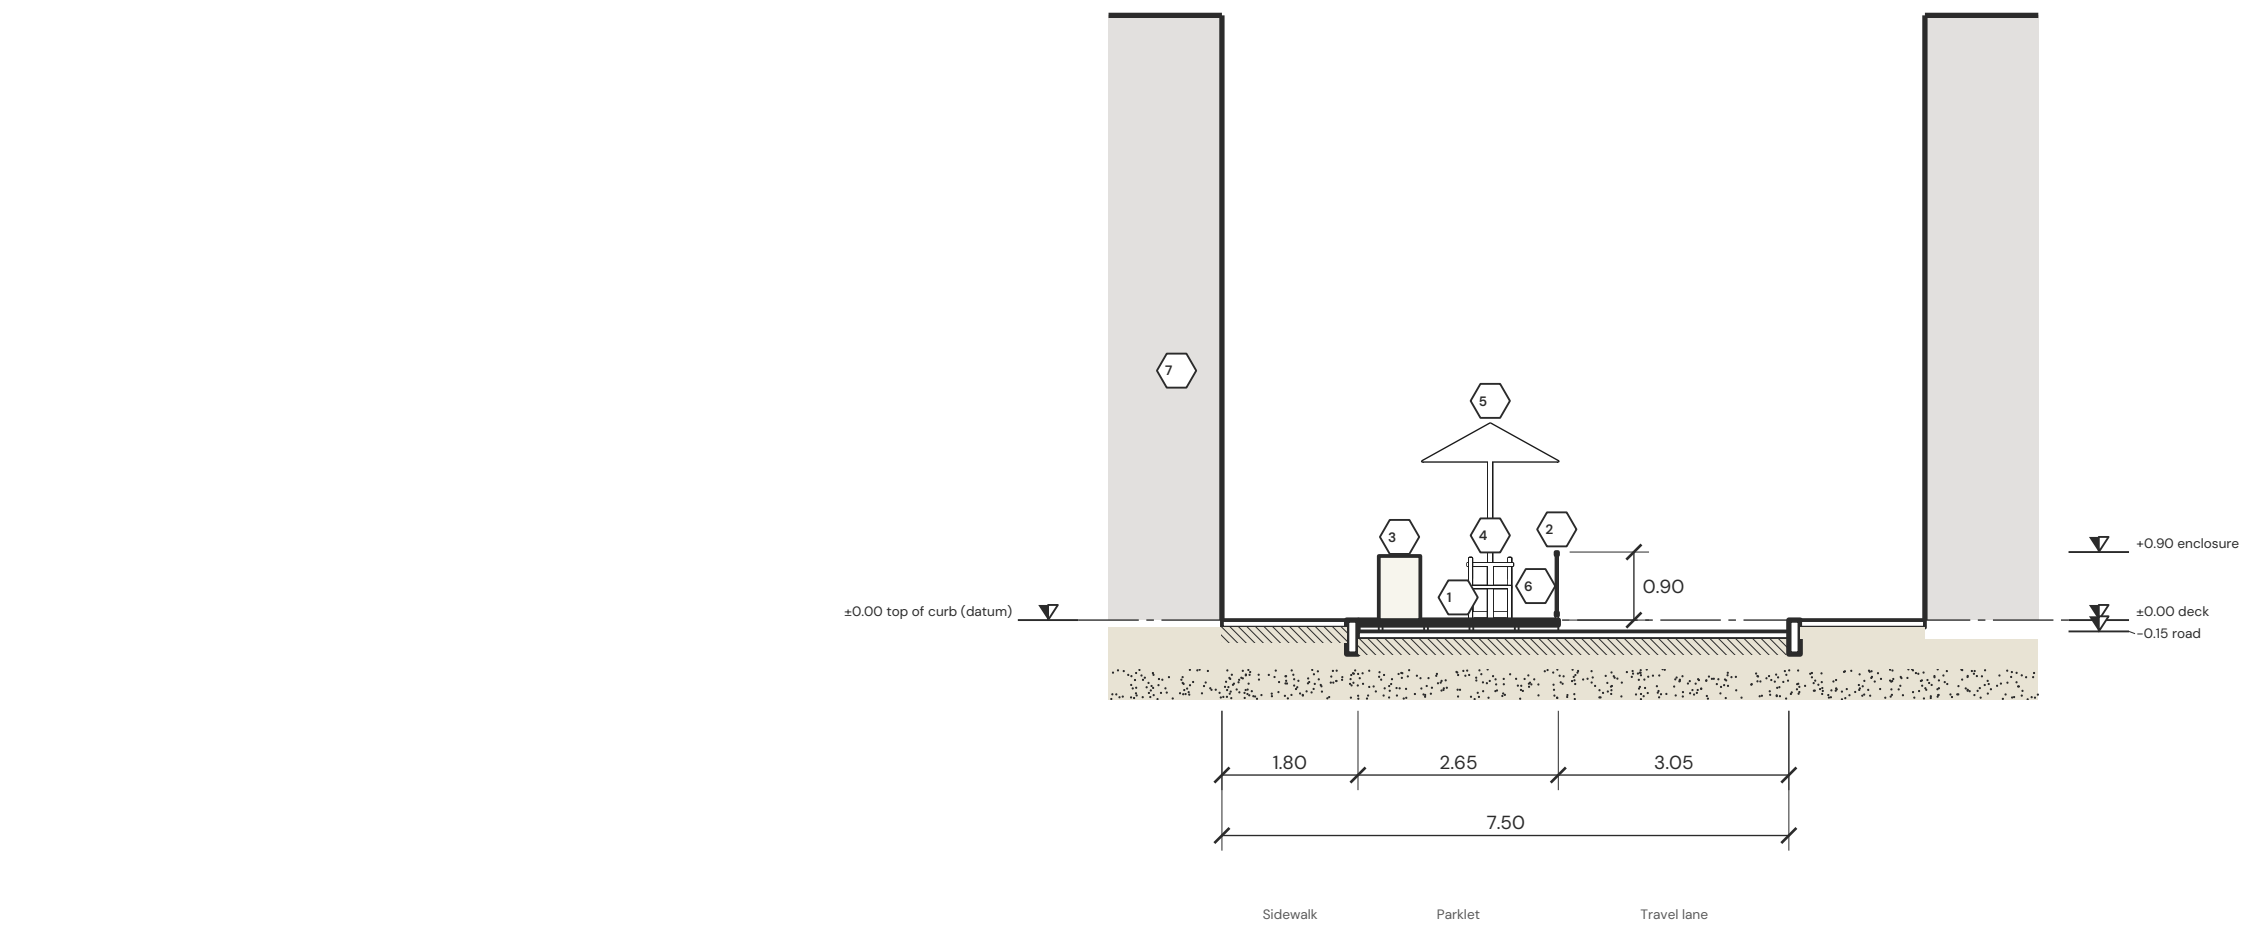

Notes

– Street section A–A at z 9.90 m, looking –z, 6.0 m beyond in elevation; the parklet in detail on A–202.

3 Bench, black stain, 2.40 x 0.55 x 0.80 m, cut.

6 Cafe table, terrazzo, 0.60 x 0.60 x 0.75 m.

1 Deck, timber boards 145 mm wide, 65 mm, on indicative supports; top +0.15 m above the road.

4 Chair, thermowood, 0.50 x 0.55 x 0.82 m.

7 Building at the cut: no address point.


2 Enclosure, steel picket, galvanized, 0.90 m above the deck.

5 Umbrella, aluminium, 1.80 x 1.80 x 2.60 m.

– Beyond the cut: outlines, the nearer in front. Trees: flat silhouettes by form, behind everything.



A–201 Street section

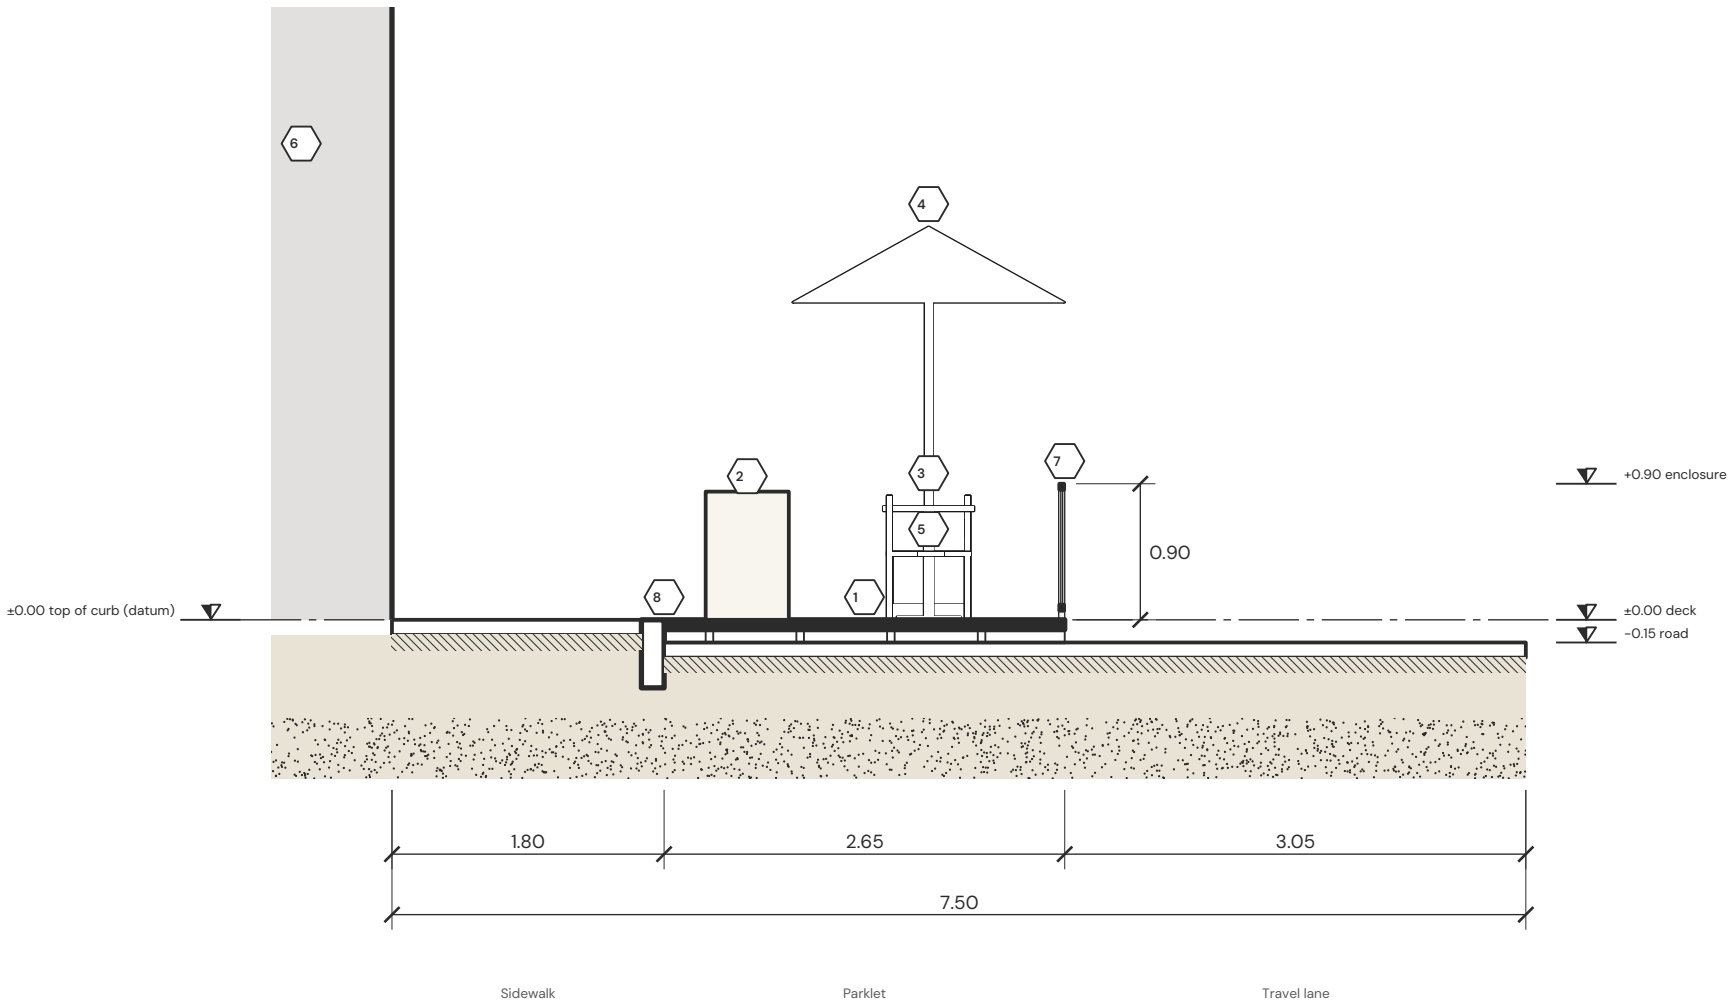

Notes

- Parklet section A-A at z 9.90 m, looking -z, 6.0 m beyond in elevation: the cut and the direction of the street section A-201.
- Beyond the cut: outlines, the nearer in front. Trees: flat silhouettes by form, behind everything.

3 Chair, thermowood, 0.50 x 0.55 x 0.82 m.

6 Building at the cut: no address point.

1 Deck, timber boards 145 mm wide, 65 mm, on indicative supports; top +0.15 m above the road.

4 Umbrella, aluminium, 1.80 x 1.80 x 2.60 m.

7 Enclosure: steel picket (bar 12 mm, bars at 100 mm, post 40 mm, posts at 1000 mm), 0.90 m above the deck, set 0.00 m in from the traffic-side edge (the buffer); C17.

2 Bench, black stain, 2.40 x 0.55 x 0.80 m, cut.

5 Cafe table, terrazzo, 0.60 x 0.60 x 0.75 m.

8 Deck edge at the sidewalk: gap 12 mm max; a larger gap takes a connector plate 13 mm max (C14, Parklet Manual p. 62).



S-001 FURNITURE SCHEDULE

| Tag   | Item                   | Size l x d x h     | Material                                                    | Count | Source            |
|-------|------------------------|--------------------|-------------------------------------------------------------|-------|-------------------|
| F1    | Bench 2.4 m, with back | 2.40 x 0.55 x 0.80 | frame: Black steel; seat: Black stain; back: Black stain    | 1     | generic archetype |
| F2    | Cafe table dia. 0.6 m  | 0.60 x 0.60 x 0.75 | frame: Black steel; top: Terrazzo                           | 1     | generic archetype |
| F3    | Chair 0.5 m            | 0.50 x 0.55 x 0.82 | frame: Galvanized; seat: Thermowood                         | 2     | generic archetype |
| F4    | Umbrella dia. 1.8 m    | 1.80 x 1.80 x 2.60 | pole: Aluminium; canopy: Fabric, canvas; base: Precast grey | 1     | generic archetype |
| F5    | Planter 1.2 m          | 1.20 x 0.60 x 0.60 | body: Galvanized                                            | 1     | generic archetype |
| F6    | Bike rack 0.9 m        | 0.90 x 0.04 x 0.80 | frame: Galvanized                                           | 1     | generic archetype |
| Total |                        | 6 types            |                                                             | 7     |                   |

Tags F1, F2 ... mark each piece on the deck plan A-103 and the layout plan A-102. Sizes in metres from each piece's parameters (the numbers the 3D and the plans draw).

Enclosure

| Side         | Archetype    | Height | Run x depth   | Materials       | See-through |
|--------------|--------------|--------|---------------|-----------------|-------------|
| Traffic side | Steel picket | 0.90 m | 19.80 x 0.040 | Galvanized      | 85 %        |
| Start end    | Planter wall | 0.90 m | 2.61 x 0.500  | Corten, Foliage | 30 %        |
| Far end      | Planter wall | 0.90 m | 2.61 x 0.500  | Corten, Foliage | 30 %        |

Buffer 0.00 m inside the deck's traffic-side edge (unusable: planting or void); usable width 2.61 m of 2.65 m. Heights above the deck; a planter's is the top of its planting (E2, Parklet Manual p. 64). In section on A-202. Buffer 0.00 m: a buffer of at least 0.30 m is recommended from a busy travel lane (Parklet Manual E2, advisory).

Parklet materials

| Part                                      | Material                       | Set by  |
|-------------------------------------------|--------------------------------|---------|
| Deck surface                              | Light timber (default deck)    | default |
| Deck edge (fascia)                        | Dark timber (default fascia)   | default |
| Enclosure posts and rails                 | each enclosure archetype's own | default |
| Enclosure infill (pickets, slats, cables) | each enclosure archetype's own | default |
| Planter boxes                             | each enclosure archetype's own | default |
| Screens                                   | each enclosure archetype's own | default |

G-002 CONSTRUCTION AND BUDGET

City of Vancouver – Parklet Manual 2016, CAD

Estimate from the Parklet Manual's 2016 figures – confirm with the City · Furniture not priced (7 pieces). Rate set: City of Vancouver – Parklet Manual 2016, CAD. Vancouver Parklet Manual, version 1.0 (June 2016): the cost range p. 18, the fees pp. 37 and 40. Figures of 2016: confirm with the City.

Quantities (from the design)

| Item                          | Qty   | Unit | How                                                                                          |
|-------------------------------|-------|------|----------------------------------------------------------------------------------------------|
| Deck area                     | 52.47 | m²   | the applied outline's area (DESIGN_MODEL.parklet.area)                                       |
| Deck perimeter                | 44.9  | m    | the sum of the outline's 4 edges                                                             |
| Joists / sleepers (run)       | 132.5 | m    | 50 joists across the deck every 0.40 m along 19.80 m, each as long as the deck is wide there |
| Decking (with waste)          | 57.72 | m²   | 52.47 m² x (1 + 10 % waste)                                                                  |
| Enclosure run (railing types) | 19.8  | m    | the runs of the rail and bench types above                                                   |
| Enclosure posts               | 20    | ea   | the posts the 3D view draws, every run                                                       |
| Planters                      | 3     | ea   | Planter wall (Start end); Planter wall (Far end); Planter 1.2 m                              |
| Planter soil                  | 0.84  | m³   | each planter's inside, length x depth x (height – 0.10 m)                                    |
| Screens                       | 0     | m    | the runs of the wall type                                                                    |
| Parking spaces taken          | 4     | ea   | 19.80 m / 6.0 m a space, rounded up (6.0 m is our estimate; the Manual gives none)           |

Estimate

| Item                                          | Qty | Unit          | Cost, CAD           | Source                                                                           |
|-----------------------------------------------|-----|---------------|---------------------|----------------------------------------------------------------------------------|
| Design, construction and installation         | 4   | parking space | \$40,000 – \$60,000 | Manual p. 18 (2016): "typically" per parking space, by design, size and material |
| Application review fee                        | 1   | once          | \$204               | Manual p. 37 (2016)                                                              |
| Program cost recovery fee                     | 1   | once          | \$1,000             | Manual p. 40 (2016)                                                              |
| Site inspection, before and after             | 1   | once          | \$200               | Manual p. 40 (2016)                                                              |
| Parking meter removal                         | 0   | meter         | \$0                 | Manual p. 40 (2016), if applicable                                               |
| Annual renewal fee (each year after)          | 1   | year          | \$500 a year        | Manual pp. 19, 40 (2016); yearly, not in the build total                         |
| Bench 2.4 m, with back (2.40 x 0.55 x 0.80 m) | 1   | each          | – (not priced)      | not priced                                                                       |
| Cafe table dia. 0.6 m (0.60 x 0.60 x 0.75 m)  | 1   | each          | – (not priced)      | not priced                                                                       |
| Chair 0.5 m (0.50 x 0.55 x 0.82 m)            | 2   | each          | – (not priced)      | not priced                                                                       |
| Umbrella dia. 1.8 m (1.80 x 1.80 x 2.60 m)    | 1   | each          | – (not priced)      | not priced                                                                       |
| Planter 1.2 m (1.20 x 0.60 x 0.60 m)          | 1   | each          | – (not priced)      | not priced                                                                       |
| Bike rack 0.9 m (0.90 x 0.04 x 0.80 m)        | 1   | each          | – (not priced)      | not priced                                                                       |
| Estimate, build and fees                      |     |               | \$41,404 – \$61,404 | 7 furniture piece(s) not priced, not counted                                     |

City of Vancouver fees: enter from the current fee schedule (<https://vancouver.ca/streets-transportation/parklets.aspx>). Wheel stops, bollards, no-stopping signs and the parklet sign are supplied by the City (Manual p. 48). An estimate to plan a budget, not a quote.

C-001 COMPLIANCE

19 pass · 0 fail · 0 not confirmed

Checks, failures first

| Rule | Manual reference                     | Requirement                                                                    | Measured value   | Result |
|------|--------------------------------------|--------------------------------------------------------------------------------|---|--------|
| C01  | Parklet Manual p. 20                 | All-day parking permitted (no rush-hour, bus, taxi, or loading zone)           | No restrictions — all-day parking confirmed.                                                                                               | PASS   |
| C02  | Parklet Manual p. 20; EDM Table 8-10 | Adjacent travel lane ≥ 3.0 m (3.2 m for bus/truck routes)                      | 1 lane × 3.050 m ≥ 3.0 m.   | PASS   |
| C03  | Parklet Manual p. 20                 | Minimum 6 m setback from nearest intersection / crosswalk edge                 | 9 m ≥ 6 m minimum. Passes.   | PASS   |
| C04  | Parklet Manual p. 20                 | Street running slope ≤ 5%                                                      | 2% ≤ 5%. Passes.   | PASS   |
| C05  | Parklet Manual p. 21                 | Minimum 5 m clearance on either side of any fire hydrant                       | 12 m ≥ 5 m minimum. Passes.; value entered, not drawn                                                                                      | PASS   |
| C06  | Parklet Manual p. 62                 | Minimum 1.5 m setback from adjacent driveways or lanes                         | 8 m ≥ 1.5 m minimum. Passes.; value entered, not drawn                                                                                     | PASS   |
| C07  | Parklet Manual p. 21                 | Minimum 1 m clearance from poles (2.4 m if trolley wires attached)             | 4 m ≥ 1.0 m (standard pole). Passes.; value entered, not drawn                                                                             | PASS   |
| C08  | Parklet Manual p. 21                 | Minimum 2 m clearance from traffic signal controller boxes / electrical kiosks | 14 m ≥ 2 m minimum. Passes.; value entered, not drawn                                                                                      | PASS   |
| C09  | Parklet Manual p. 21                 | Minimum 1 m clearance from manhole lids, valves, grates, access chambers       | 5 m ≥ 1 m minimum. Passes.; value entered, not drawn                                                                                       | PASS   |
| C10  | Parklet Manual p. 21                 | Does not block Fire Dept. connections, utility connections, or fire exits      | No blockages confirmed. Passes.; value entered, not drawn                                                                                  | PASS   |
| C11  | Parklet Manual p. 21                 | Curb and roadside drainage maintained — street drains not blocked              | Drainage confirmed clear and channel designed in. Passes.; value entered, not drawn                                                        | PASS   |
| C12  | Parklet Manual p. 20                 | Minimum pedestrian clearances on boulevard / utility strip maintained          | Boulevard not used. Criterion not triggered. Passes.                                                                                       | PASS   |
| C13  | Parklet Manual p. 62                 | Minimum 1.5 m setback from adjacent parking spaces                             | 2 m ≥ 1.5 m minimum. Passes.   | PASS   |
| C14  | Parklet Manual p. 62                 | Deck flush with the sidewalk (gap at most 12 mm; connector at most 13 mm)      | Deck flush with the curb, 12 mm gap (12 mm max). Passes.                                                                                   | PASS   |
| C15  | Parklet Manual p. 62                 | Deck load capacity ≥ 7.2 kPa                                                   | 7.5 kPa ≥ 7.2 kPa minimum. Passes.   | PASS   |
| C16  | Parklet Manual p. 60                 | Accessible route 1.5 m clear from an entry, 1.5 m turning space                | 3 routes 1.50 m clear or more from the entries to the cafe table, the bench end; 1.50 m turning space at each entry, turn and end. Passes. | PASS   |
| C17  | Parklet Manual p. 64                 | Enclosure 0.75–1.0 m high on the traffic side and both ends                    | traffic side 0.90 m (steel picket), ends 0.90 / 0.90 m: within 0.75–1.0 m. Passes.                                                         | PASS   |
| C18  | Parklet Manual p. 65                 | At least two unobstructed openings of 1.8 m or more to the sidewalk            | 7 openings of 1.8 m or more to the sidewalk (clear runs 4.45, 0.15, 0.15, 1.85, 8.20 m). Passes.                                           | PASS   |
| C19  | Parklet Manual p. 65                 | Overhead elements at least 2.1 m clear above the deck and within the footprint | umbrella 2.10 m clear: at least 2.1 m and within the footprint. Passes.                                                                    | PASS   |

Advisory (no numbered check)

| Advisory                                                                                  | Detail   |
|-------------------------------------------------------------------------------------------|---|
| Deck 2.65 m wide – Parklet Manual: typically 2.3–2.5 m; wider to be confirmed by the City | Parklet Manual p. 20 and P2, p. 62: the adjacent lane rule leads to a deck of 2.3–2.5 m; the City confirms the maximum width. |

Lane envelope, EDM Table 8-10: travel lane widths (m); this design's route in bold

| Route           | Lane role        | Absolute min. | Preferred   | Max.        |
|-----------------|------------------|---------------|-------------|-------------|
| <b>Standard</b> | <b>rightmost</b> | <b>2.80</b>   | <b>3.00</b> | <b>3.40</b> |
| <b>Standard</b> | <b>other</b>     | <b>2.70</b>   | <b>3.00</b> | <b>3.20</b> |
| <b>Standard</b> | <b>single</b>    | <b>2.90</b>   | <b>3.00</b> | <b>3.50</b> |
| Bus / truck     | rightmost        | 3.00          | 3.20        | 3.50        |
| Bus / truck     | other            | 3.00          | 3.20        | 3.20        |
| Bus / truck     | single           | 3.50          | 3.50        | 3.60        |

Route of this design: standard. Rightmost = the lane next to the parklet (or its bike lane / buffer); single = a lone travel lane. Below preferred needs City Engineer approval (note 4); above maximum is an exception only (note 8), never beyond 4.8 m.

C-001 Compliance

C-001 COMPLIANCE (CONT.)

19 pass · 0 fail · 0 not confirmed

Beside the parklet (from the Section): the travel lane. Bike lane: none. The rightmost travel lane (3.05 m) is the first beyond the parklet.

Street changes: existing (as imported) against proposed (the Section)

No imported street is recorded: import the street context to compare the Section with it.

This design (m)

| Lane | Direction | Role   | Width | Abs. min. | Preferred | Max. | Band                       | C02 min. | C02  |
|------|-----------|--------|-------|-----------|-----------|------|----------------------------|----------|------|
| 1    | one-way   | single | 3.05  | 2.90      | 3.00      | 3.50 | within preferred – maximum | 3.00     | PASS |

C02 (Parklet Manual p. 20): the adjacent travel lane stays at least 3.0 m (3.2 m on bus / truck routes). Widths are the Section's travel-lane segments.

S-002    SITE SURVEY

values to confirm on site

Confirm on site

Measure each item on site and write the value in the last column; enter them in Curbside with the survey template (Site > Survey), or import a survey point file.

| Item                                      | Value now | Source   | Measured |
|-------------------------------------------|-----------|----------|----------|
| Sidewalk width, frontage to curb face     | 1.80 m    | estimate |          |
| Curb-to-curb width                        | 5.70 m    | estimate |          |
| parklet width                             | 2.65 m    | model    |          |
| travel lane width                         | 3.05 m    | model    |          |
| Street slope along the curb (C04)         | 2 %       | entered  |          |
| Nearest hydrant to the deck (C05)         | 12 m      | entered  |          |
| Nearest driveway to the deck (C06)        | 8 m       | entered  |          |
| Nearest pole to the deck (C07)            | 4 m       | entered  |          |
| Nearest signal box to the deck (C08)      | 14 m      | entered  |          |
| Nearest manhole / valve to the deck (C09) | 5 m       | entered  |          |
| Nearest intersection / crosswalk (C03)    | 9 m       | entered  |          |

X-001 SOURCES

| Standards and data                                         |   |
|------------------------------------------------------------|---|
|                                                            |   |
| Source                                                     | Used for   |
| City of Vancouver, Parklet Manual, Version 1.0 (June 2016) | criteria C01 – C15 and their pages   |
| Parklet Manual E2, p. 64                                   | C17: the enclosure 0.75 – 1.0 m high on the traffic side and both ends; the 0.30 m buffer advised from a busy travel lane (advisory)                                                                                          |
| Parklet Manual E3, p. 65                                   | C18: at least two unobstructed openings of 1.8 m or more to the sidewalk   |
| Parklet Manual E5, p. 65                                   | C19: overhead elements at least 2.1 m clear above the deck and within the footprint   |
| Parklet Manual E4, p. 64; G13                              | a solid edge flagged for the City to confirm (advisory)   |
| City of Vancouver, Engineering Design Manual (2026)        | Table 8–10 travel lane widths (8.7.3.1, pp. 275–277); bike lane and buffer widths (8.5.4.5)   |
| City of Vancouver Standard Detail Drawings                 | W4.1 fire hydrant clearance; WW1 manhole; E5.19C utility pole; E1.3 signal controller base   |
| City of Vancouver street standards placement guidance      | street furniture offsets   |
| Parklet Manual G19, p. 60                                  | accessible route 1.5 m clear and a 1.5 m turning area (C16; the 1.1 m route of the BC Building Code, 3.8, noted and not used)                                                                                                 |
| Rate set: City of Vancouver – Parklet Manual 2016, CAD     | Vancouver Parklet Manual, version 1.0 (June 2016): the cost range p. 18, the fees pp. 37 and 40. Figures of 2016: confirm with the City. (G-002)                                                                              |
| Visualisation 1: Street view                               | AI-assisted, indicative; Nano Banana Pro (2K), rendered 2026–09–25; 49.5 mm lens, 29 deg to the deck axis. Rendered with the author’s Replicate account for this sample; your own renders use the key you add in Connections. |
| Visualisation 2: Sidewalk view                             | AI-assisted, indicative; Nano Banana Pro (2K), rendered 2026–09–25; 49.5 mm lens, 20 deg to the deck axis. Rendered with the author’s Replicate account for this sample; your own renders use the key you add in Connections. |
| Visualisation 3: Corner view                               | AI-assisted, indicative; Nano Banana Pro (2K), rendered 2026–09–25; 49.5 mm lens, 6 deg to the deck axis. Rendered with the author’s Replicate account for this sample; your own renders use the key you add in Connections.  |
| Visualisation 4: Aerial view                               | AI-assisted, indicative; Nano Banana Pro (2K), rendered 2026–09–25; isometric, as the axonometric. Rendered with the author’s Replicate account for this sample; your own renders use the key you add in Connections.         |
| DM Sans (SIL Open Font License 1.1)                        | the report's typeface, embedded   |
| jsPDF, svg2pdf.js (MIT)                                    | the PDF engine (tools/vendor)   |

| Entered inputs                                             |                                             |
|------------------------------------------------------------|---------------------------------------------|
|                                                            |                                             |
| Input                                                      | Value                                       |
| Parking restrictions at this location                      | No restrictions — all-day parking permitted |
| Is the adjacent lane a bus or truck route?                 | Standard traffic lane only                  |
| Distance to nearest crosswalk / intersecting sidewalk edge | 9 m                                         |
| Street running slope at this block                         | 2 %                                         |
| Distance to nearest fire hydrant (each side)               | 12 m                                        |
| Distance to nearest driveway or lane                       | 8 m                                         |
| Distance to nearest pole                                   | 4 m                                         |
| Trolley wires on this pole?                                | No trolley wires                            |
| Distance to nearest signal box / electrical kiosk          | 14 m                                        |

| Entered inputs (cont.)                                                                     |                                                      |
|--------------------------------------------------------------------------------------------|------------------------------------------------------|
|                                                                                            |                                                      |
| Input                                                                                      | Value                                                |
| Distance to nearest manhole / valve / grate                                                | 5 m                                                  |
| Does the parklet footprint block any FD / utility connection or fire exit?                 | No — confirmed clear                                 |
| Are all street drains / catch basins clear of the footprint?                               | Yes — all drains clear; drainage channel designed in |
| Does the parklet use the boulevard strip, and if so, are pedestrian clearances maintained? | Boulevard not used — stays within parking lane only  |
| Setback from adjacent parking space / meter (each end)                                     | 2 m                                                  |
| Designed load capacity                                                                     | 7.5 kPa                                              |

| From the design model  |   |
|------------------------|---|
|                        |   |
| Value                  | Derived from   |
| Travel lane widths     | the Section editor’s travel-lane segments against EDM Table 8–10 (3.05 m)   |
| Deck area              | the rectangle footprint, 52.47 m2   |
| Compliance             | each check’s own result for the inputs above; an input not entered leaves its check not confirmed   |
| Seats, route, entries  | the generator’s metrics of the current layout (access model)   |
| Enclosure, deck levels | DESIGN_MODEL.enclosure (steel picket in galvanized, 0.90 m high on the traffic side, at the deck edge; planter wall at both ends) and PARKLET_LEVELS, the numbers the 3D, the render and these drawings share |

| Assumptions                                      |   |
|--------------------------------------------------|---|
|                                                  |   |
| Topic                                            | Assumption   |
| Furniture positions                              | the model's; not field-measured   |
| Buildings                                        | heights and depths are entered or imported estimates, for context only                                                                                                  |
| Wheel stops and bollards                         | City-supplied; drawn nominally in the 1.5 m parking setback   |
| C18 openings                                     | a single clear run of w m along the sidewalk edge, between the end enclosures and 1.5 m deep, counts floor(w / 1.8) openings (Parklet Manual E3: at least two of 1.8 m) |
| End planters (design saved before the enclosure) | End planters raised to 0.90 m planter walls to meet Parklet Manual E2 (0.75–1.0 m)                                                                                      |
| Host building programme                          | not entered: the default (cafe, glazed frontage) is used for the renders, the prompts and the Generate bias                                                             |
| Library dimensions                               | those marked DI are interpreted, not source data   |
| Drawings                                         | schematic, for the pre-application: not construction drawings; no structural or construction feasibility is assessed                                                    |

X-001 Sources